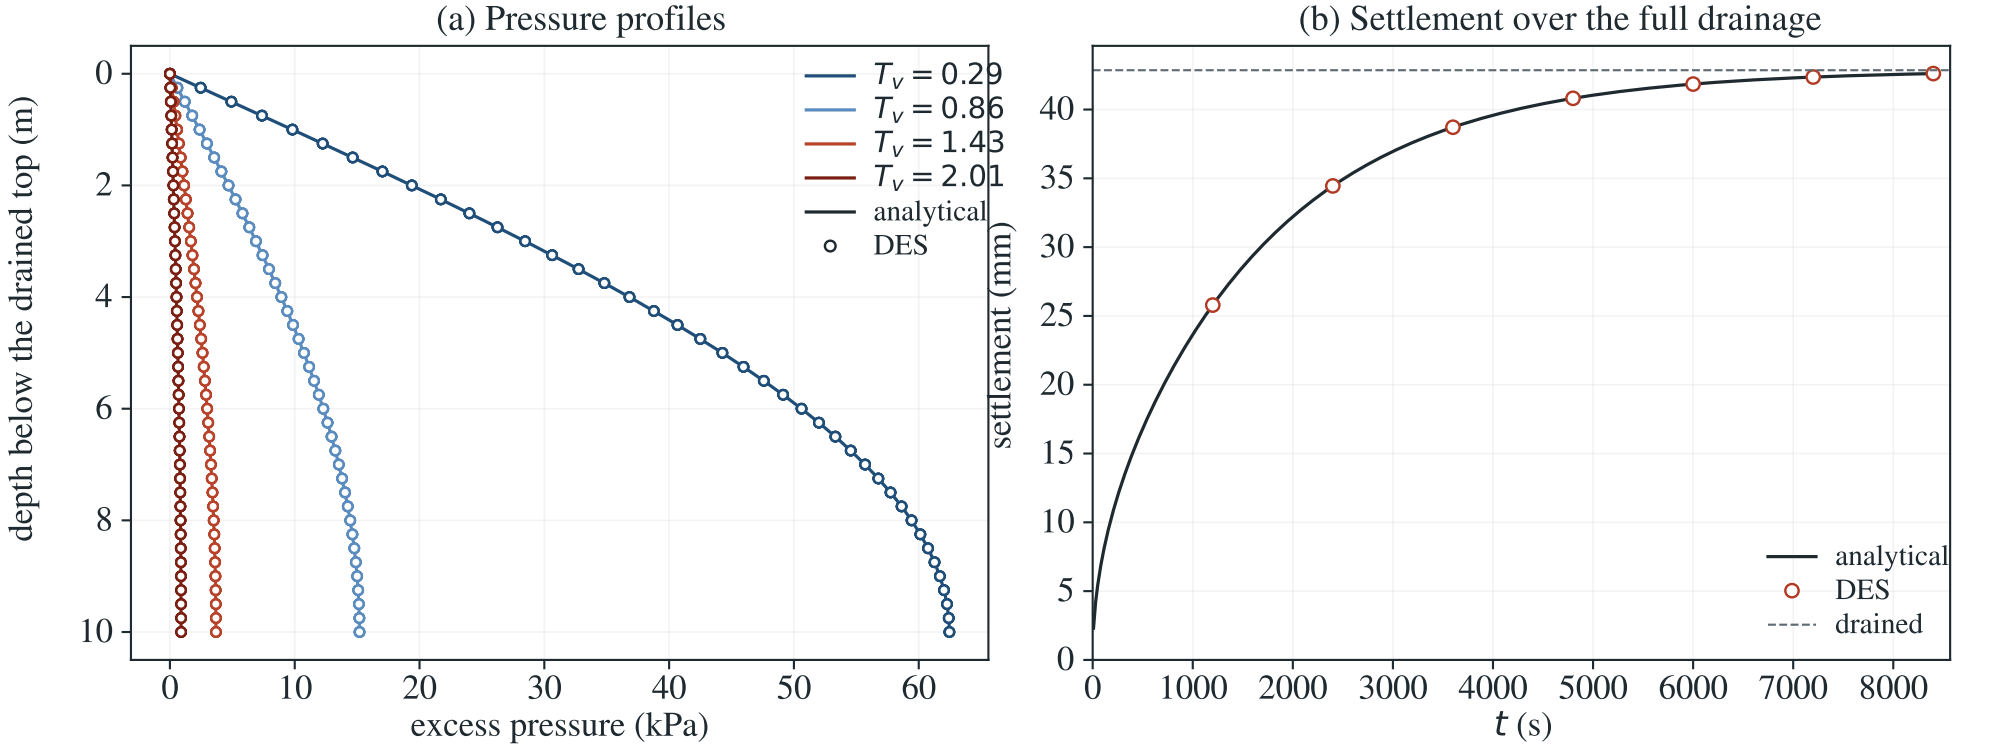

(a) Pressure profiles
depth below the drained top (m)
excess pressure (kPa)
$T_v = 0.29$
$T_v = 0.86$
$T_v = 1.43$
$T_v = 2.01$
analytical
DES
(b) Settlement over the full drainage
settlement (mm)
t (s)
analytical
DES
drained