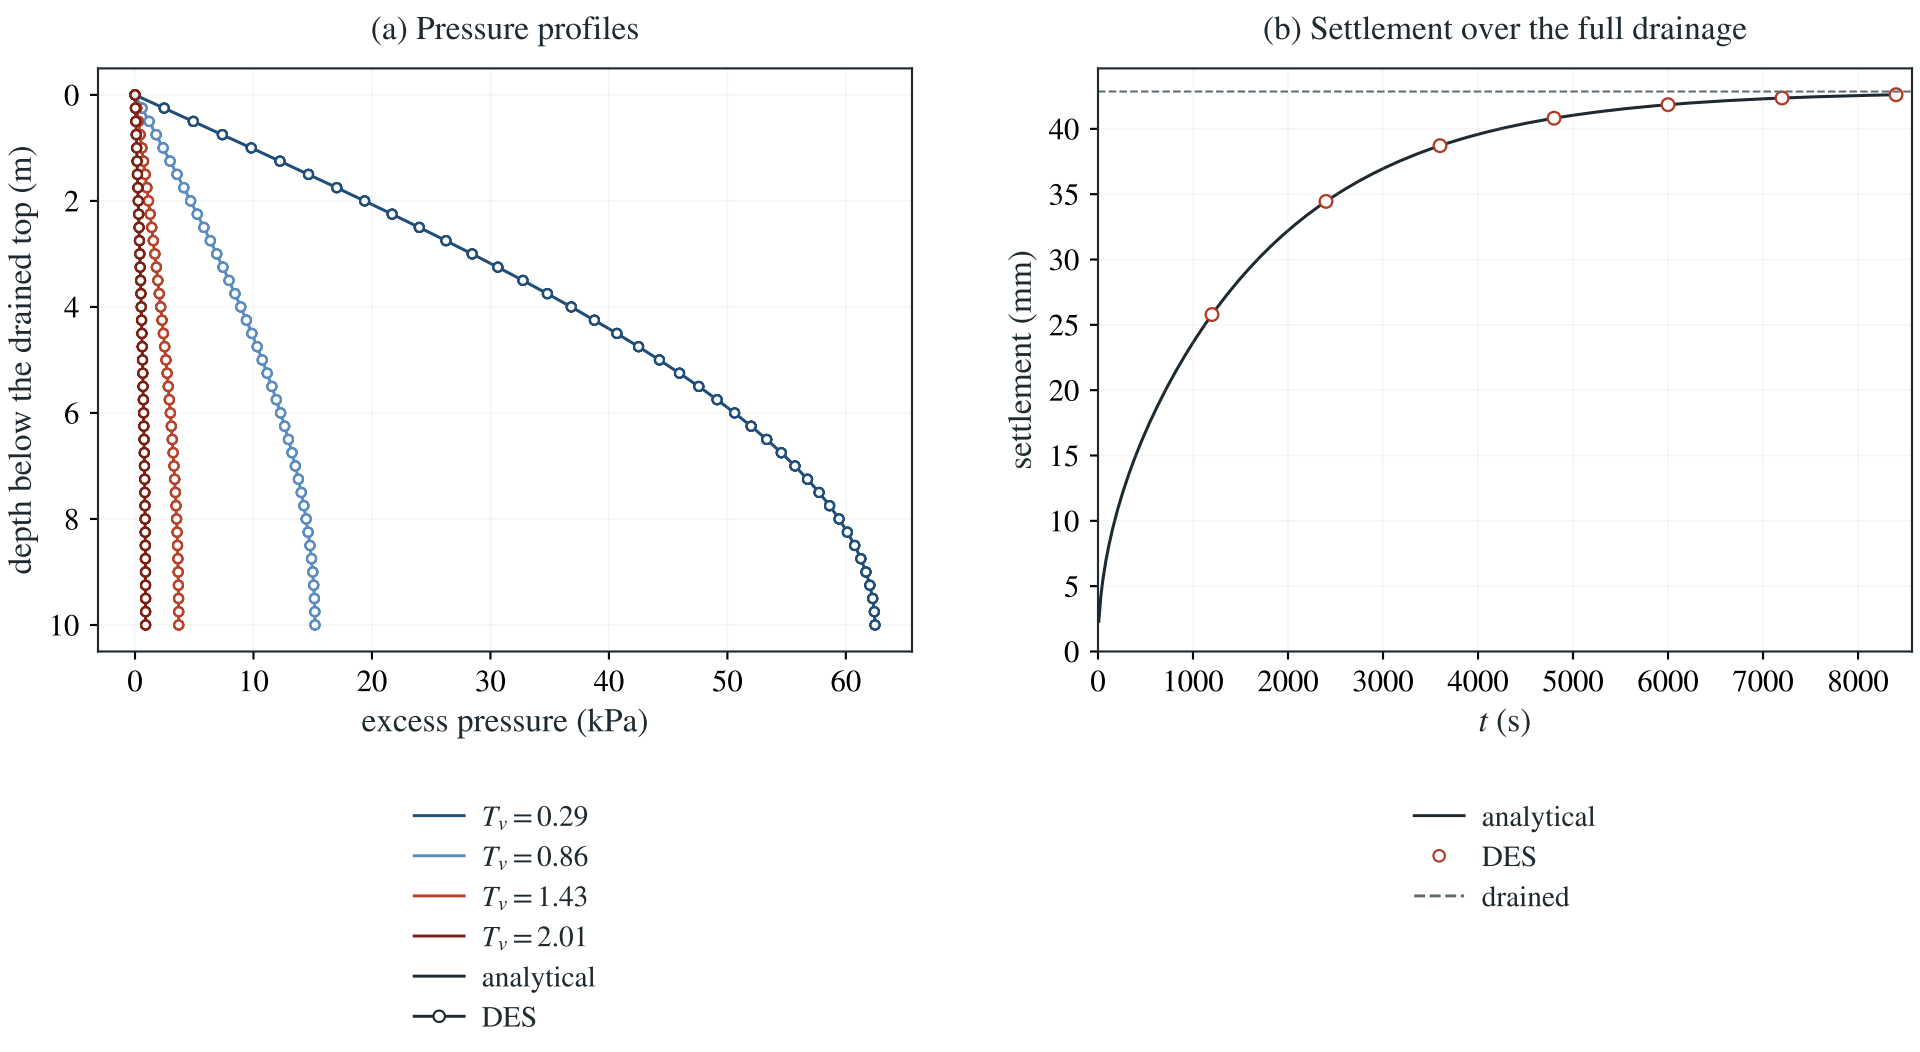

(a) Pressure profiles
depth below the drained top (m)
0
2
4
6
8
10
0
10
20
30
40
50
60
excess pressure (kPa)
$T_v = 0.29$
$T_v = 0.86$
$T_v = 1.43$
$T_v = 2.01$
analytical
DES
(b) Settlement over the full drainage
settlement (mm)
0
5
10
15
20
25
30
35
40
0
1000
2000
3000
4000
5000
6000
7000
8000
t (s)
analytical
DES
drained